
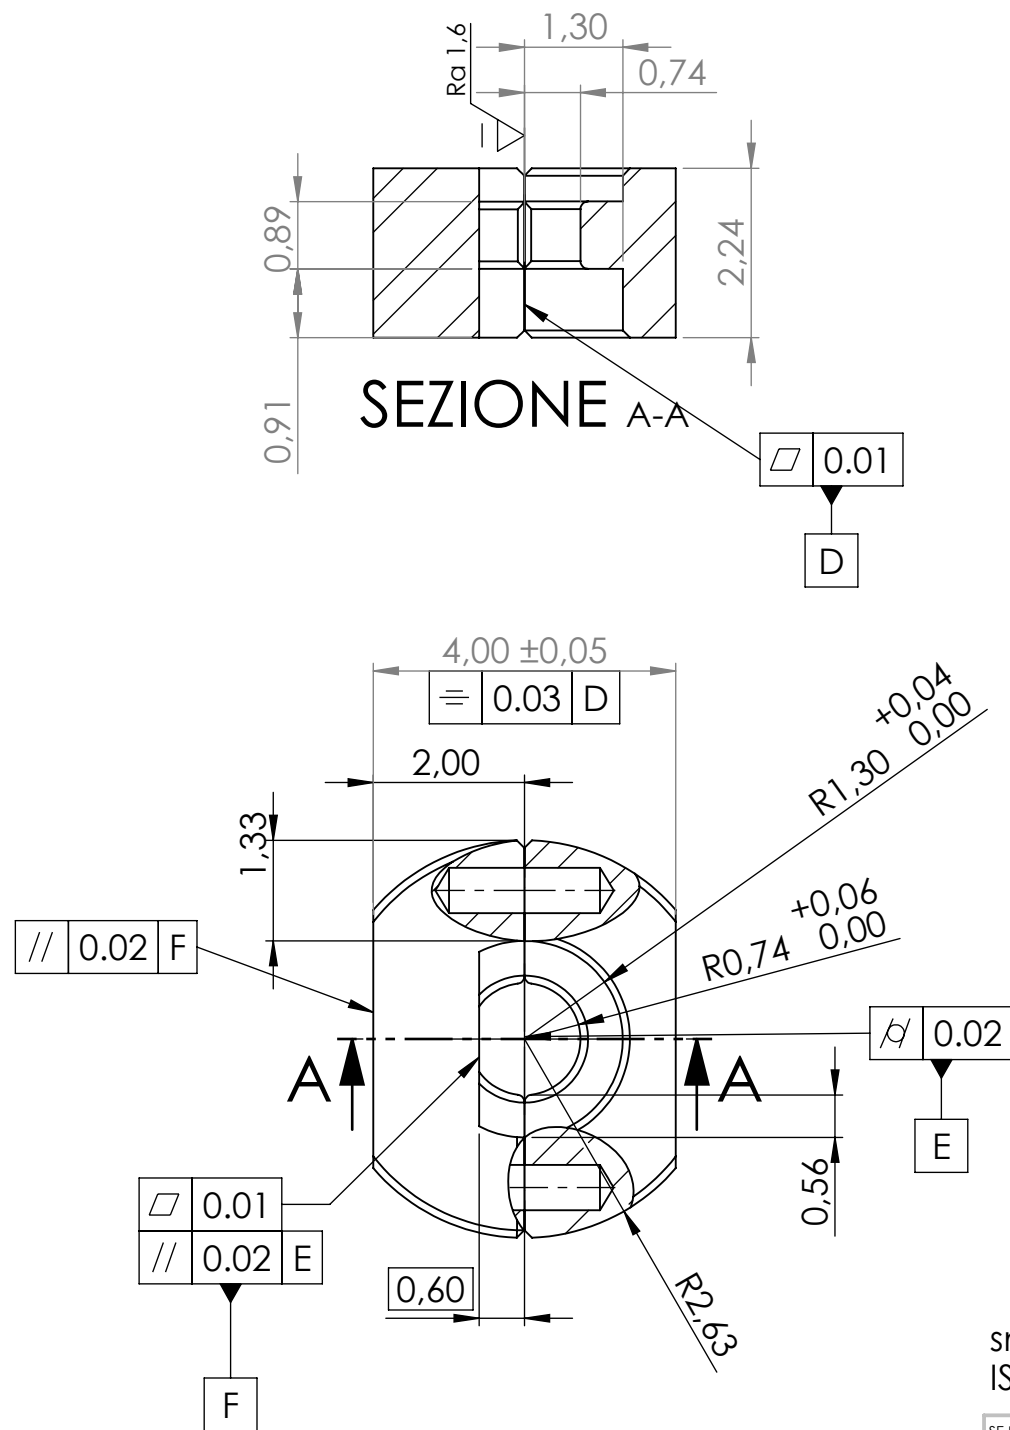


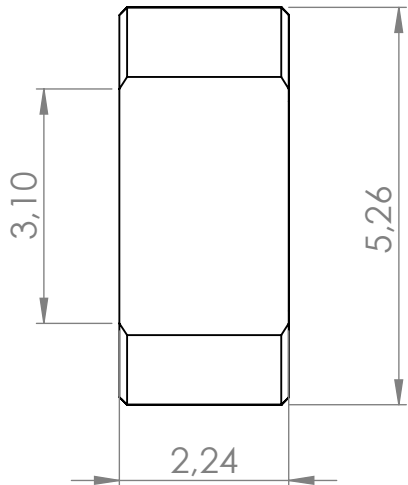

SEZIONE A-A

smussi e raccordi non quotati R 0,1 0,1x45°
ISO 2768-mk

SE NON SPECIFICATO: QUOTE IN MILLIMETRI FINITURA SUPERFICIE: TOLLERANZE: LINEARE: ANGOLARE:		FINITURA:		INTERRUZIONE BORDI NETTI		NON SCALARE DISEGNO		REVISIONE	
NOME		FIRMA		DATA		TITOLO:			
DISEG.									
VERIF.									
APPR.									
FABB.									
Qual.						MATERIALE: AISI 304		N. DISEGNO	
								Clamshell	
								A3	
						PESO:		SCALA:10:1	
								FOGLIO 1 DI 1	