


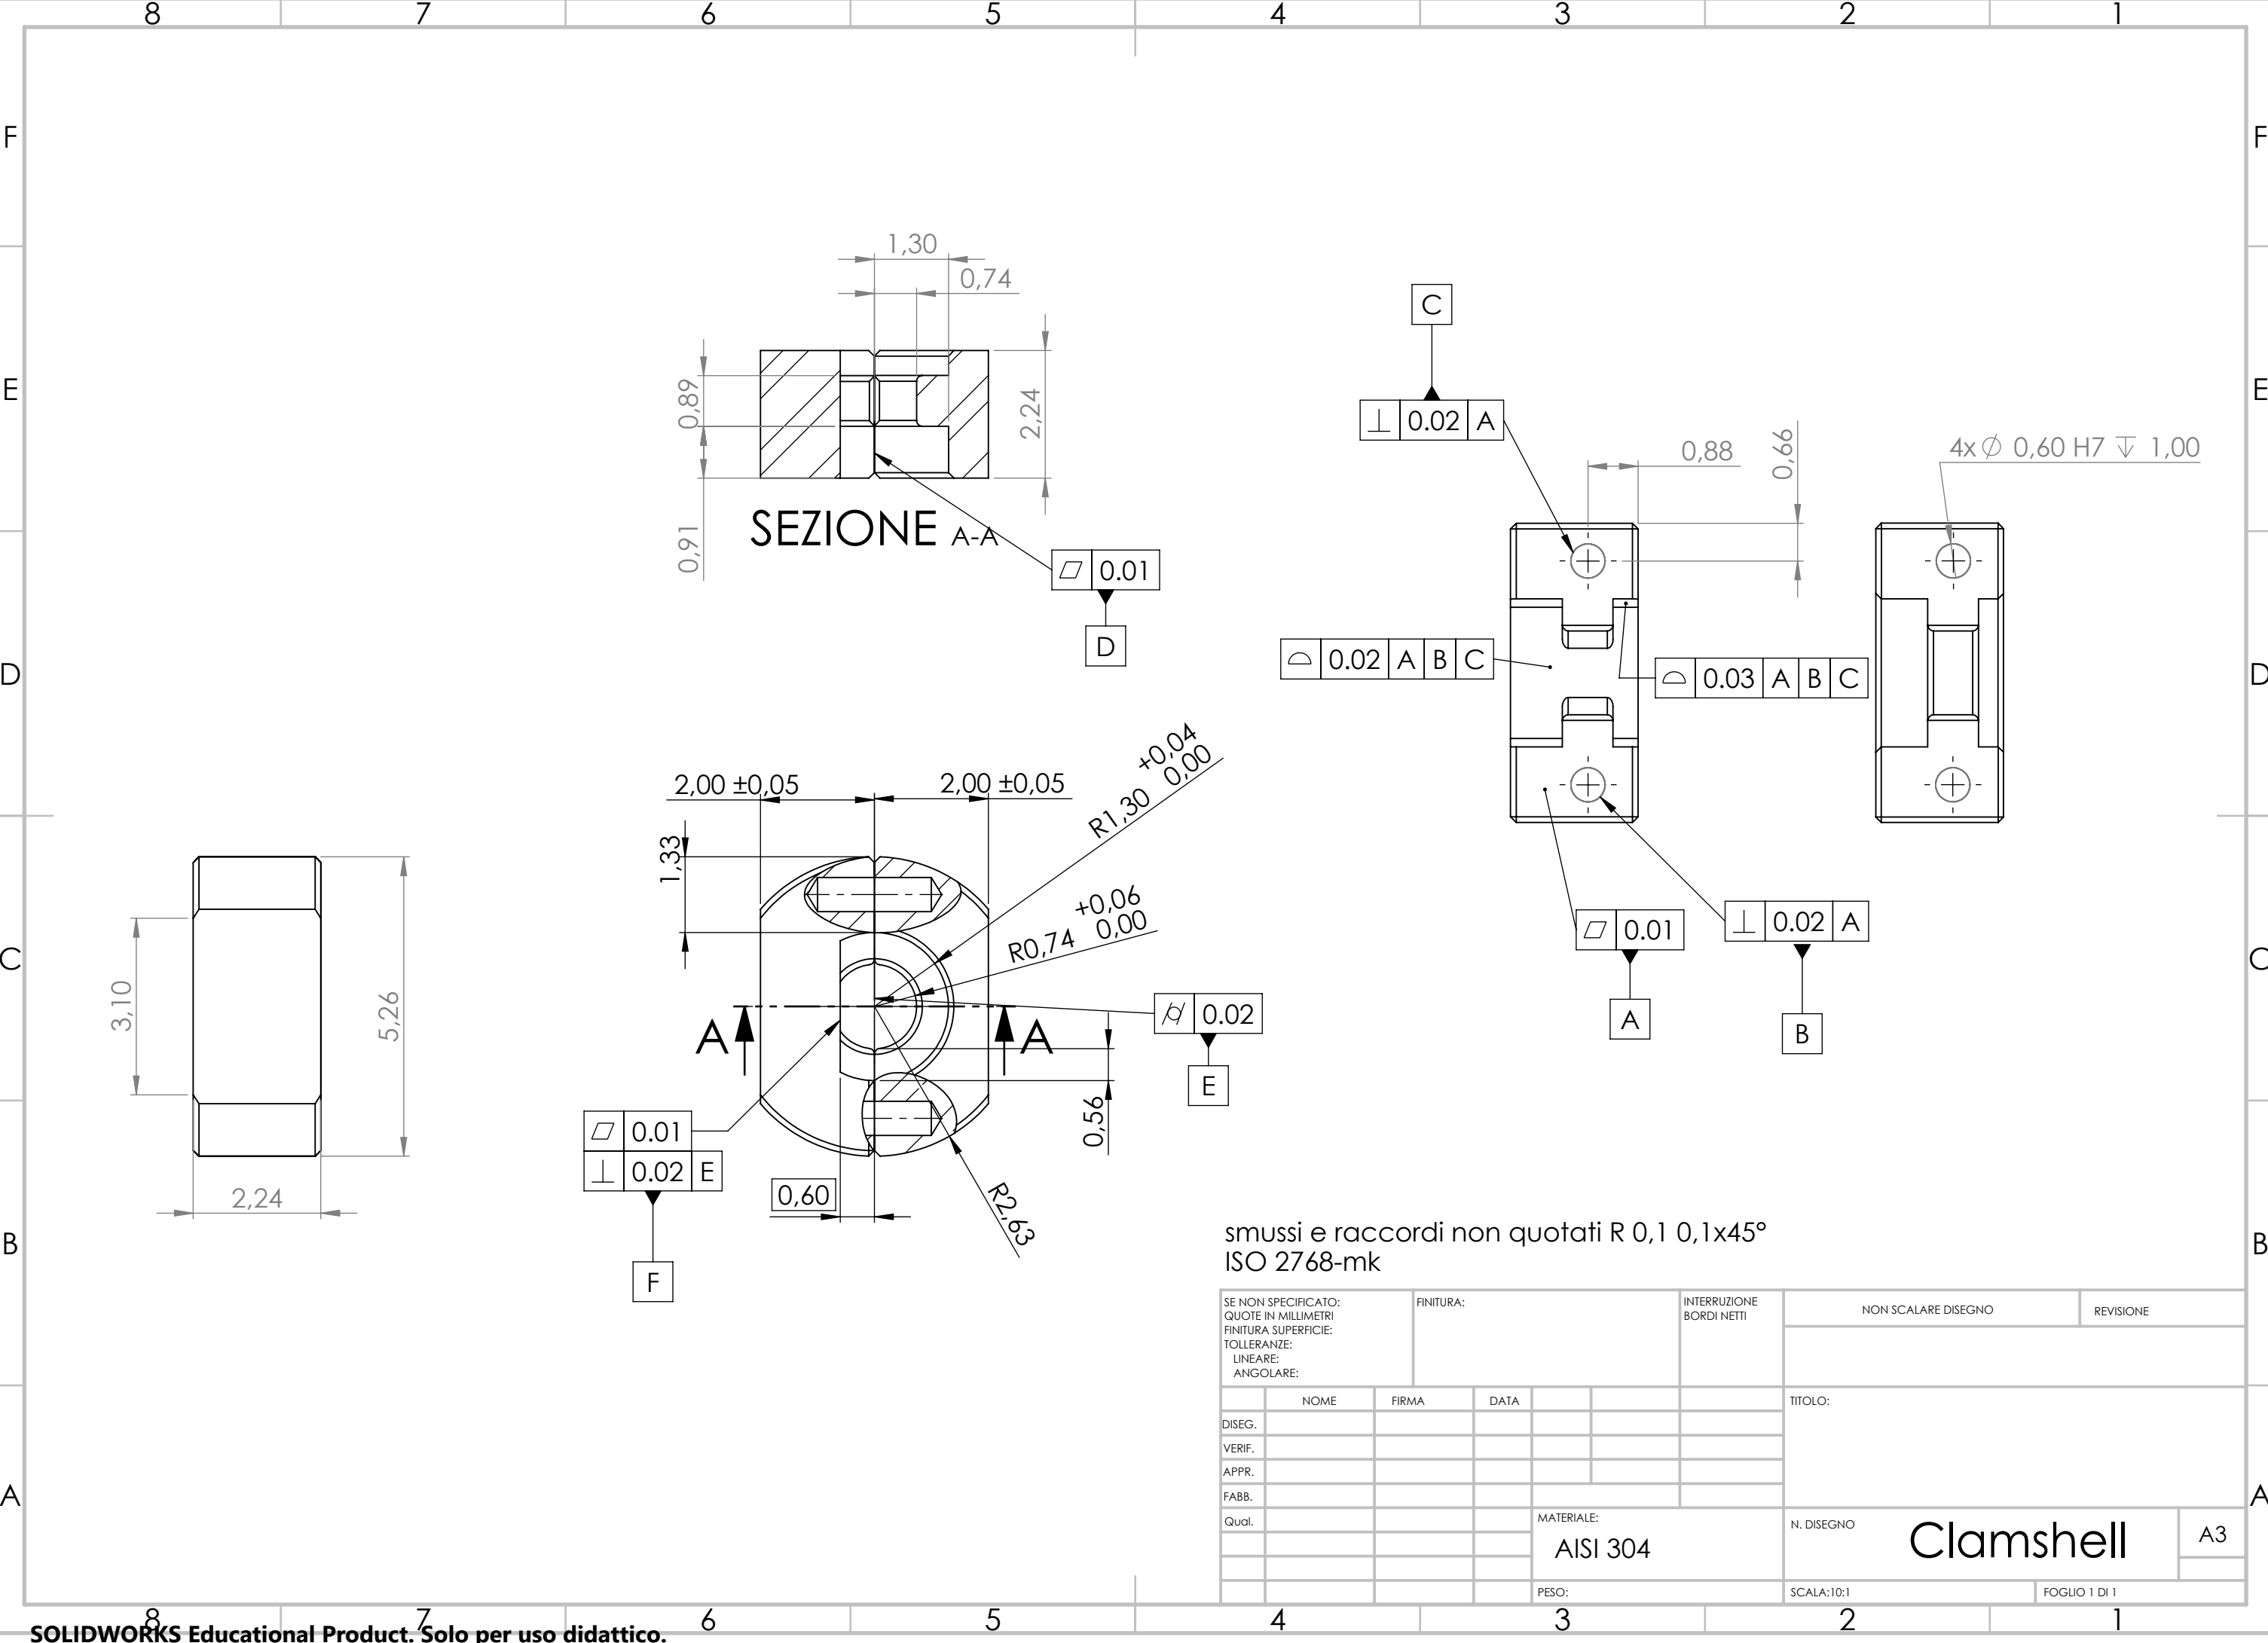

SEZIONE A-A

smussi e raccordi non quotati R 0,1 0,1x45°
ISO 2768-mk

SE NON SPECIFICATO: QUOTE IN MILLIMETRI FINITURA SUPERFICIE: TOLLERANZE: LINEARE: ANGOLARE:				FINITURA:		INTERRUZIONE BORDI NETTI		NON SCALARE DISEGNO		REVISIONE
	NOME	FIRMA	DATA					TITOLO:		
DISEG.										
VERIF.										
APPR.										
FABB.										
Qual.								N. DISEGNO		A3
								SCALA:10:1		FOGLIO 1 DI 1